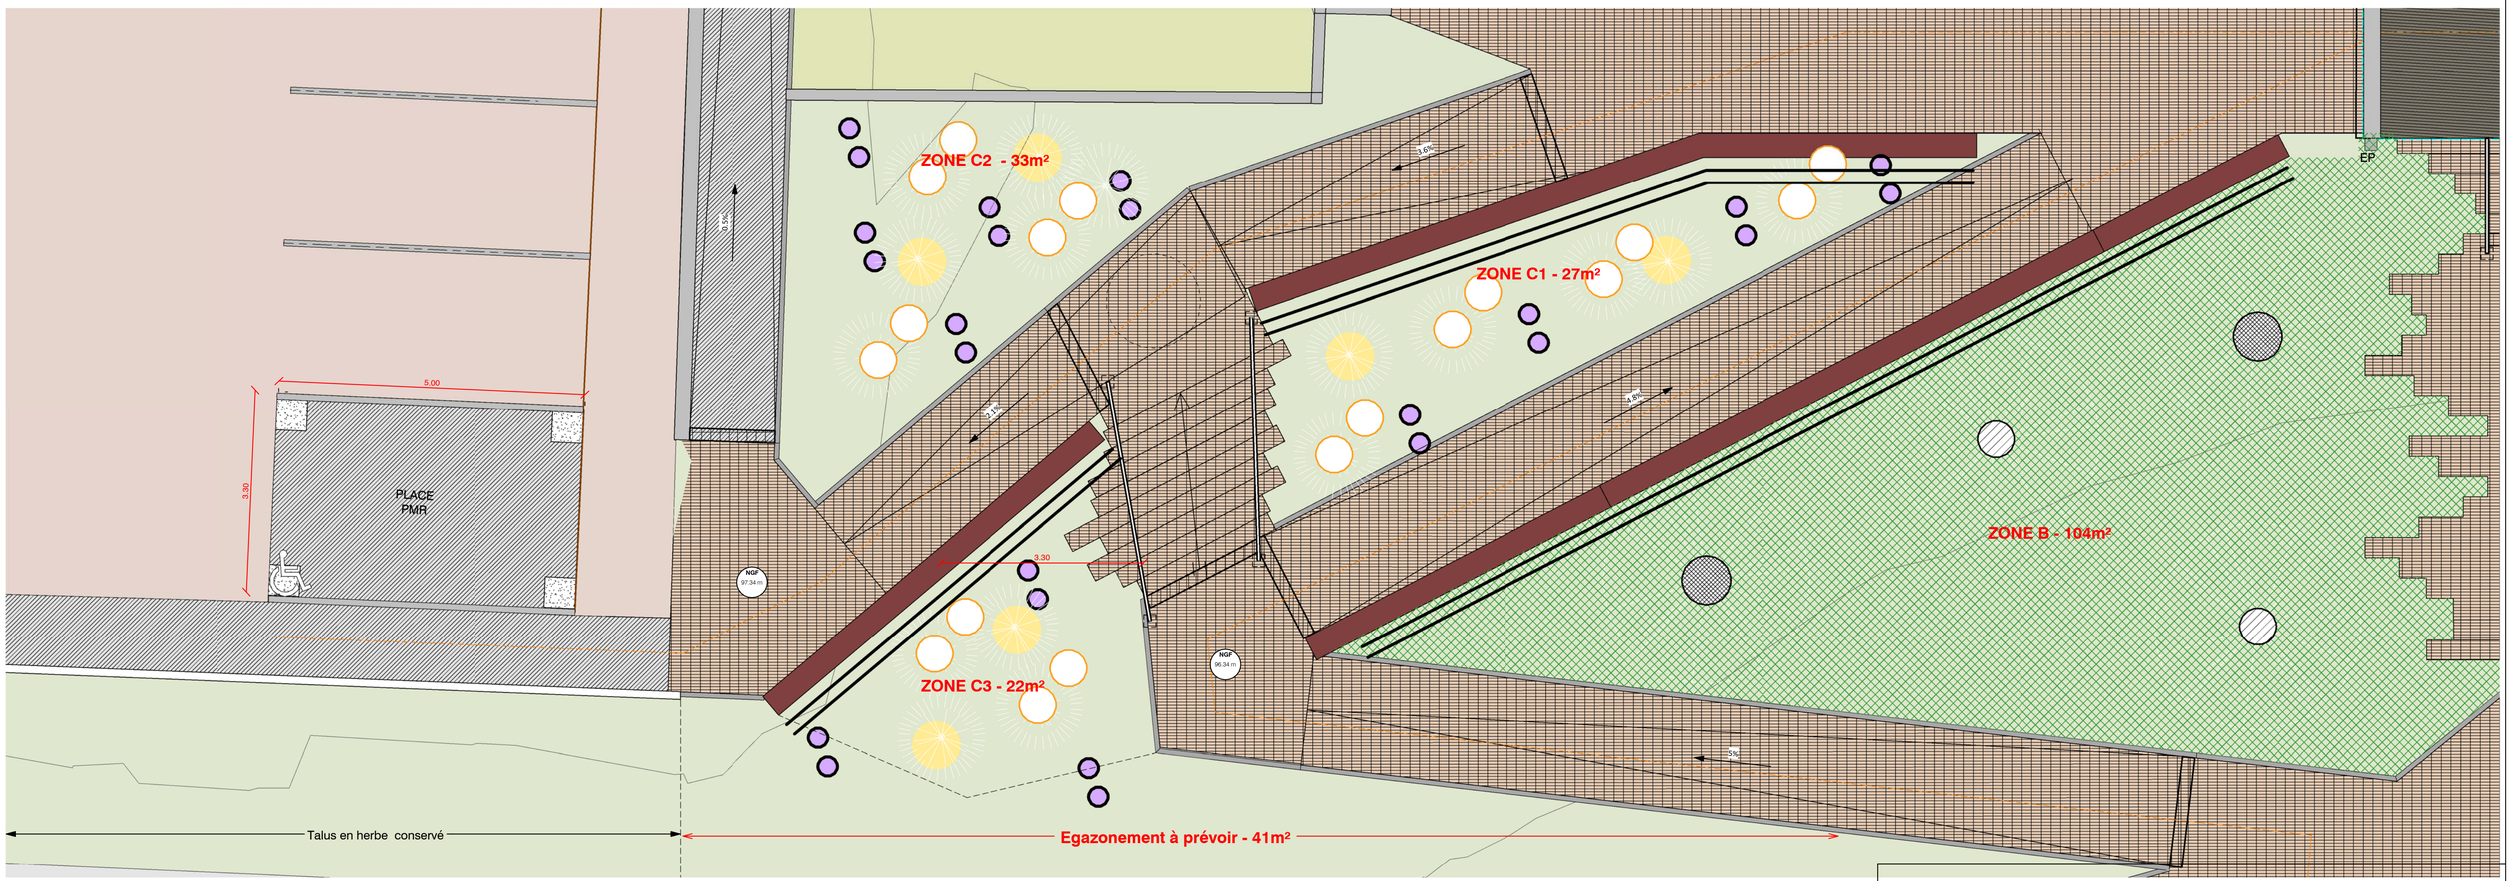


Plans de végétation zone B et C
Ech: 1 : 50

## LEGENDE :

### ARBRES :

- Saule Tortueux
- Poirier
- Pommier
- Arbre de Judée

### ARBUSTES :

- Salix purpurea "Nana"
- Ligustrum ovalifolium
- Miscanthus
- Lierre de Colchide - Hedera colchica Arborescens
- Salvia
- Phillyreau angustifolia

### PLANTES :

- Polystichum acrostichoides
- Jonc de jardinier
- Achilea
- Orchidée Purpurea
- Consoude
- Romarin
- Consude
- Jasmin étoilé (en pied de gabion)

### MELANGE :

- Lathyrus vernus et Mazus reptans
- Bugle rampante - Ajuga reptans
- Mélange de Jonquilles, narcisse et jacinthe
- Gazon espagnol

Reconversion et extension de la nouvelle mairie
18 Rue de la Lombardie, 78930 Guerville

| | | |
|---|---|---|
| MAÎTRE D'OUVRAGE | Mairie de Guerville<br>4 place de la Mairie<br>78930 Guerville | |
| ASSISTANT MAÎTRISE D'OUVRAGE | INGÉNIERY | Marion Toutin<br>M : mtoutin@yvelines.fr<br>T : 06 86 51 60 36 |
| BUREAU DE CONTRÔLE | ALPHA CONTRÔLE | M.Zanmenou<br>M : azanmenou@alphacontrole.com<br>T : 06 27 19 46 22 |
| COORDONNATEUR CSPS | QUALICONSULT | M. CATELAN<br>M : gilles.catelan@qualiconsult.fr<br>T : 06 71 70 67 17 |
| ARCHITECTE BET OPC | PALABRES ARCHITECTES<br>11 Rue Manin<br>75019 PARIS | Pascal Brunet<br>M : p.brunet@palabres.fr<br>T : 06 23 54 55 13 |
| | | |
| | | |

DCE

Plans de végétation

| ÉMETTEUR | LOT | | PHASE | TYPE | | | N°DOC | INDICE | DATE | FORMAT |
|---|---|---|---|---|---|---|---|---|---|---|
| PALABRES | ARCHI | | DCE | PLAN | | | 3.11 | A | 26/07/2024 | |

Echelle : 1 : 50