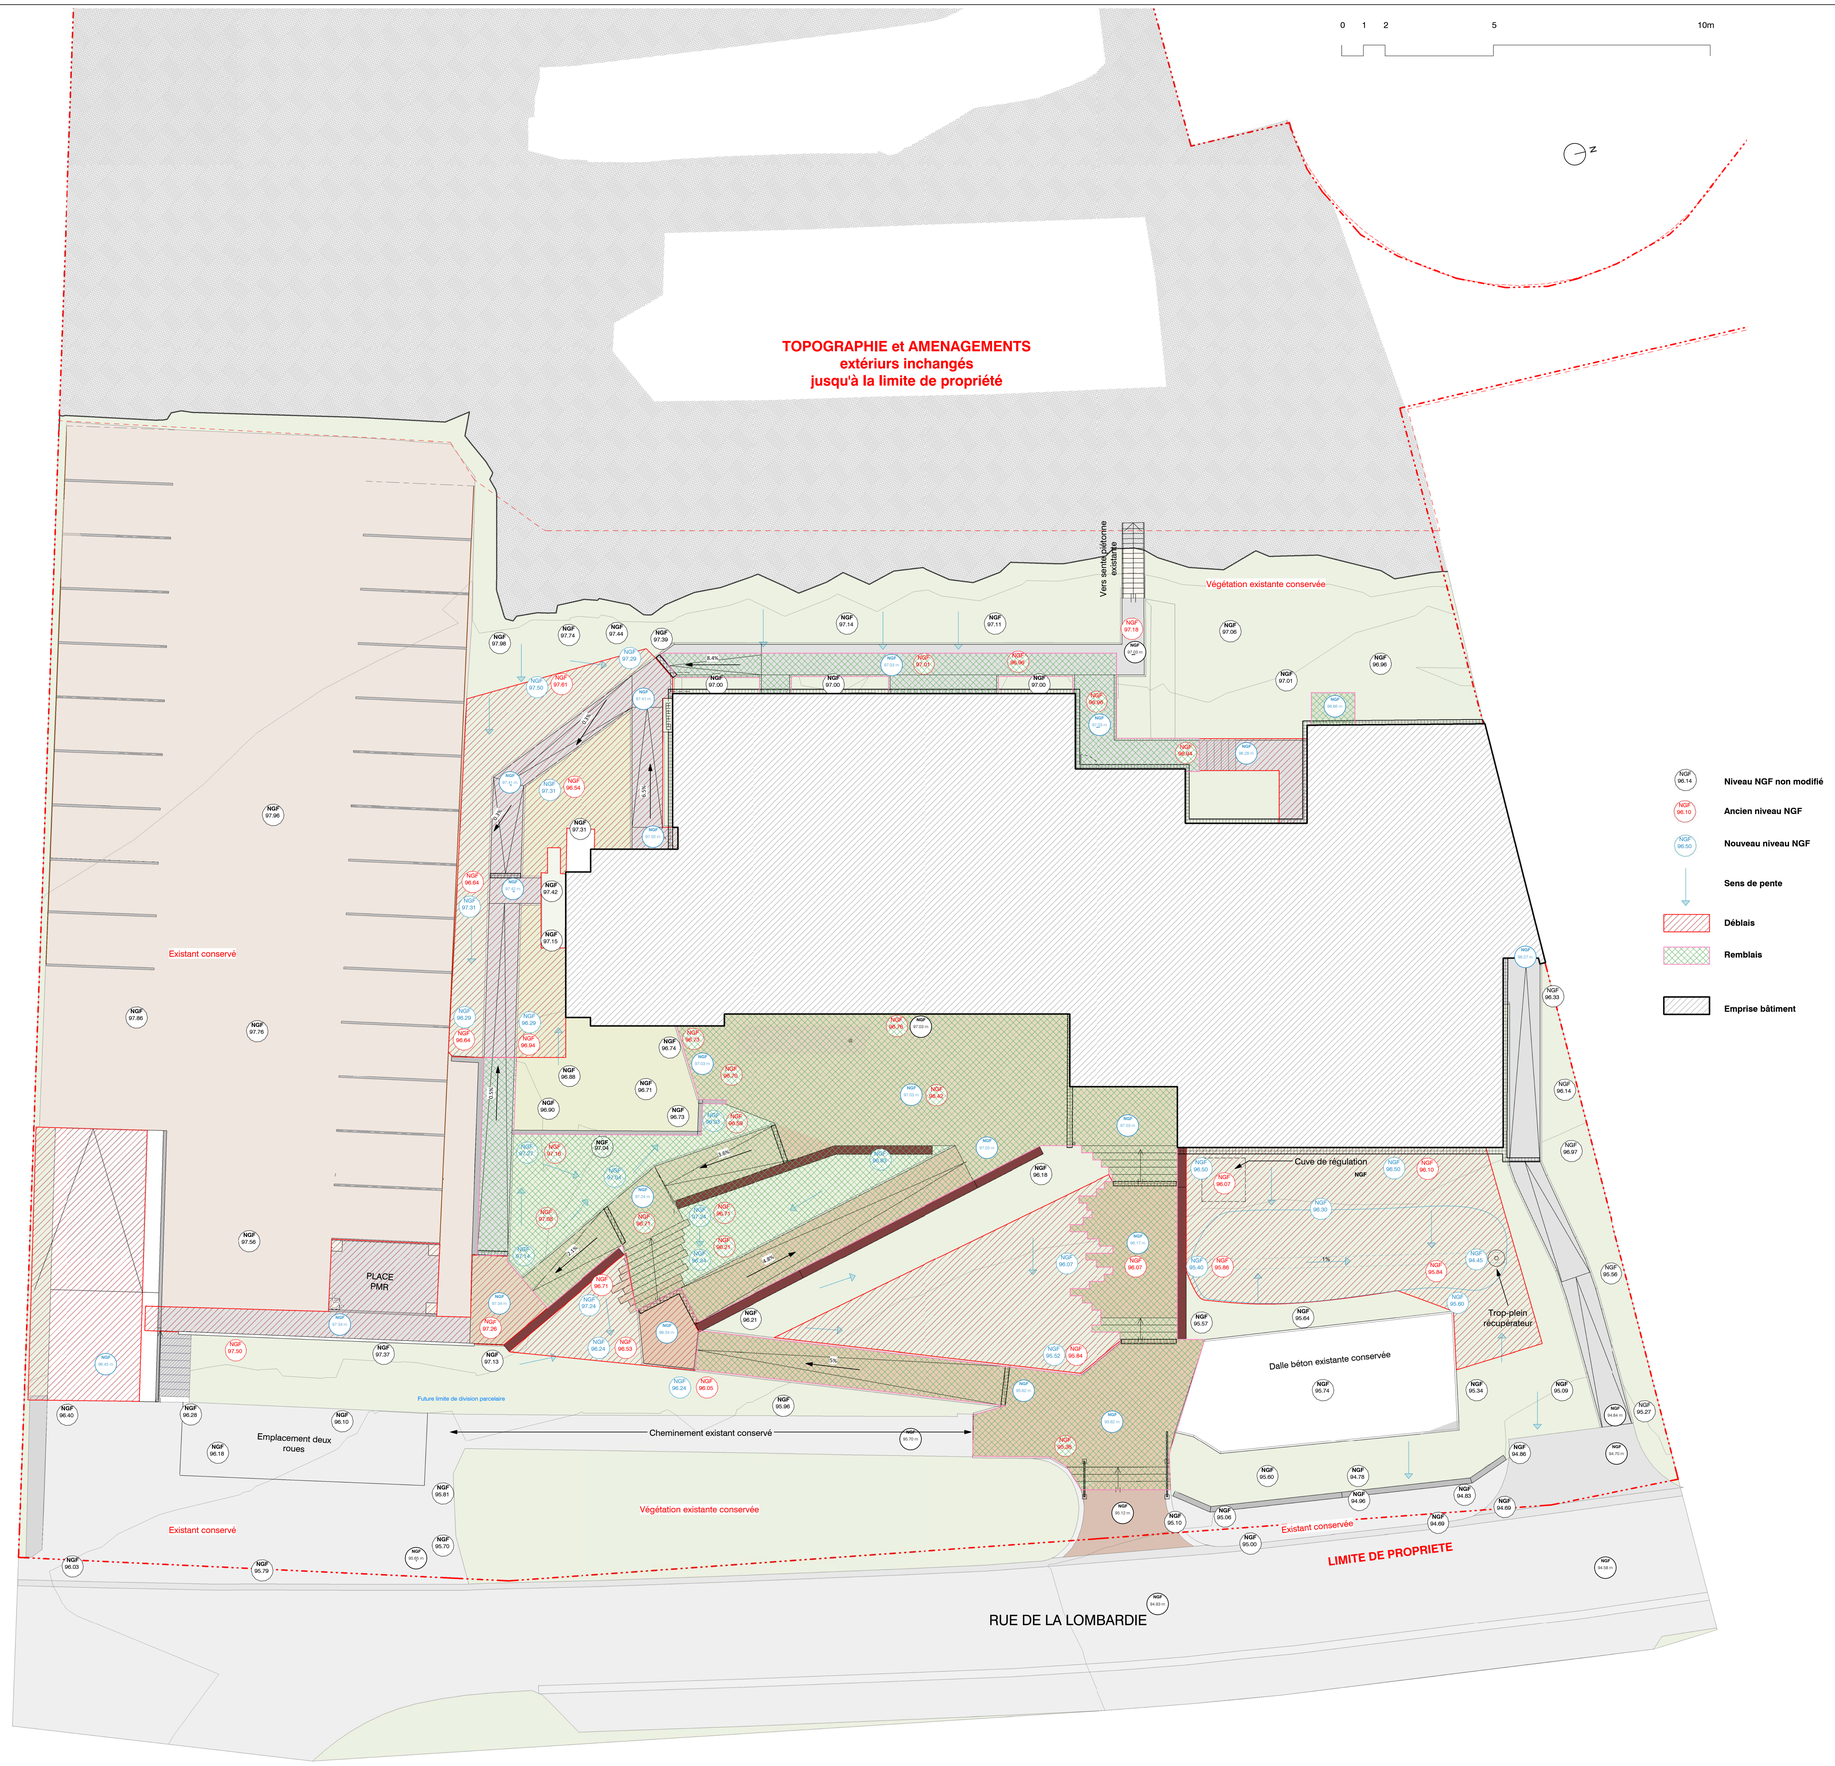

Reconversion et extension de la nouvelle mairie

18 Rue de la Lombardie, 78930 Guerville

MAÎTRE D'OUVRAGE	Mairie de Guerville 4 place de la Mairie 78930 Guerville	
ASSISTANT MAÎTRISE D'OUVRAGE	INGÉNIERY	Marion Toutin M : mtoutin@yvelines.fr T : 06 86 51 60 36
BUREAU DE CONTRÔLE	ALPHA CONTRÔLE	M.Zanmenou M : azanmenou@alphacontrole.com T : 06 27 19 46 22
COORDONNATEUR CSPS	QUALICONSULT	M. CATELAN M : gilles.catelan@qualiconsult.fr T : 06 71 70 67 17
ARCHITECTE BET OPC	PALABRES ARCHITECTES 11 Rue Manin 75019 PARIS	Pascal Brunet M : p.brunet@palabres.fr T : 06 23 54 55 13

DCE

Plans de remblais et déblais

ÉMETTEUR	LOT		PHASE	TYPE			N°DOC	INDICE	DATE	FORMAT
PALABRES	ARCHI		DCE	PLAN			3.1D	A	26/07/2024	

Echelle : 1 : 100